

Fire Fighting Working Drawings



ATA

01151313481
ataahmed937@gmail.com

FIRE FIGHTING LIST OF DRAWINGS

SHEET NAME	SHEET NUM	SCALE
SERIES - 000 GENERAL		
Fire Fighting Cover	001	-
LIST OF DRAWINGS	002	-
Project DESCRIPTION	003	-
SERIES - 100 COLOR CODE		
GROUND FLOOR PLAN - Protection Type	101	1:110
SERIES - 200 Fire Fighting Pipe Work		
GROUND FLOOR PLAN - Sprinkler System	201	1:110
GROUND FLOOR PLAN - Fire Fighting System	202	1:110
SERIES - 300 Details		
BASEMENT PLAN - PUMP ROOM	301	1:40
Pump & ZONE CONTROL VALVE Hook Ups	302	-
Hanger	303	-
SERIES - 400 SCHEDULE		
SCHEDULE	401	-

PROJECT NAME
HospitalSHEET TITLE
Fire FightingDESIGN BY
AHMED ATACHECKED BY
Ahmed M.Shuhayb
Hassan WaheedSCALE SHEET NO
1:100 H-01DATE
14-8-2023



ATA

01151313481

ataahmed937@gmail.com

Project Discretion

	location	Cairo, Egypt
	Area	2150 m ²
	No. of Floor	1
	System	Sprinkler & Hose Cabinet System

PROJECT NAME
Hospital

SHEET TITLE
Fire Fighting

DESIGN BY
AHMED ATA

CHECKED BY
Ahmed M.Shuhayb
Hassan Waheed

SCALE SHEET NO
1:100 H-01

DATE
14-8-2023

ASEC OFFICE COPYRIGHT




ATA



01151313481



ataahmed937@gmail.com

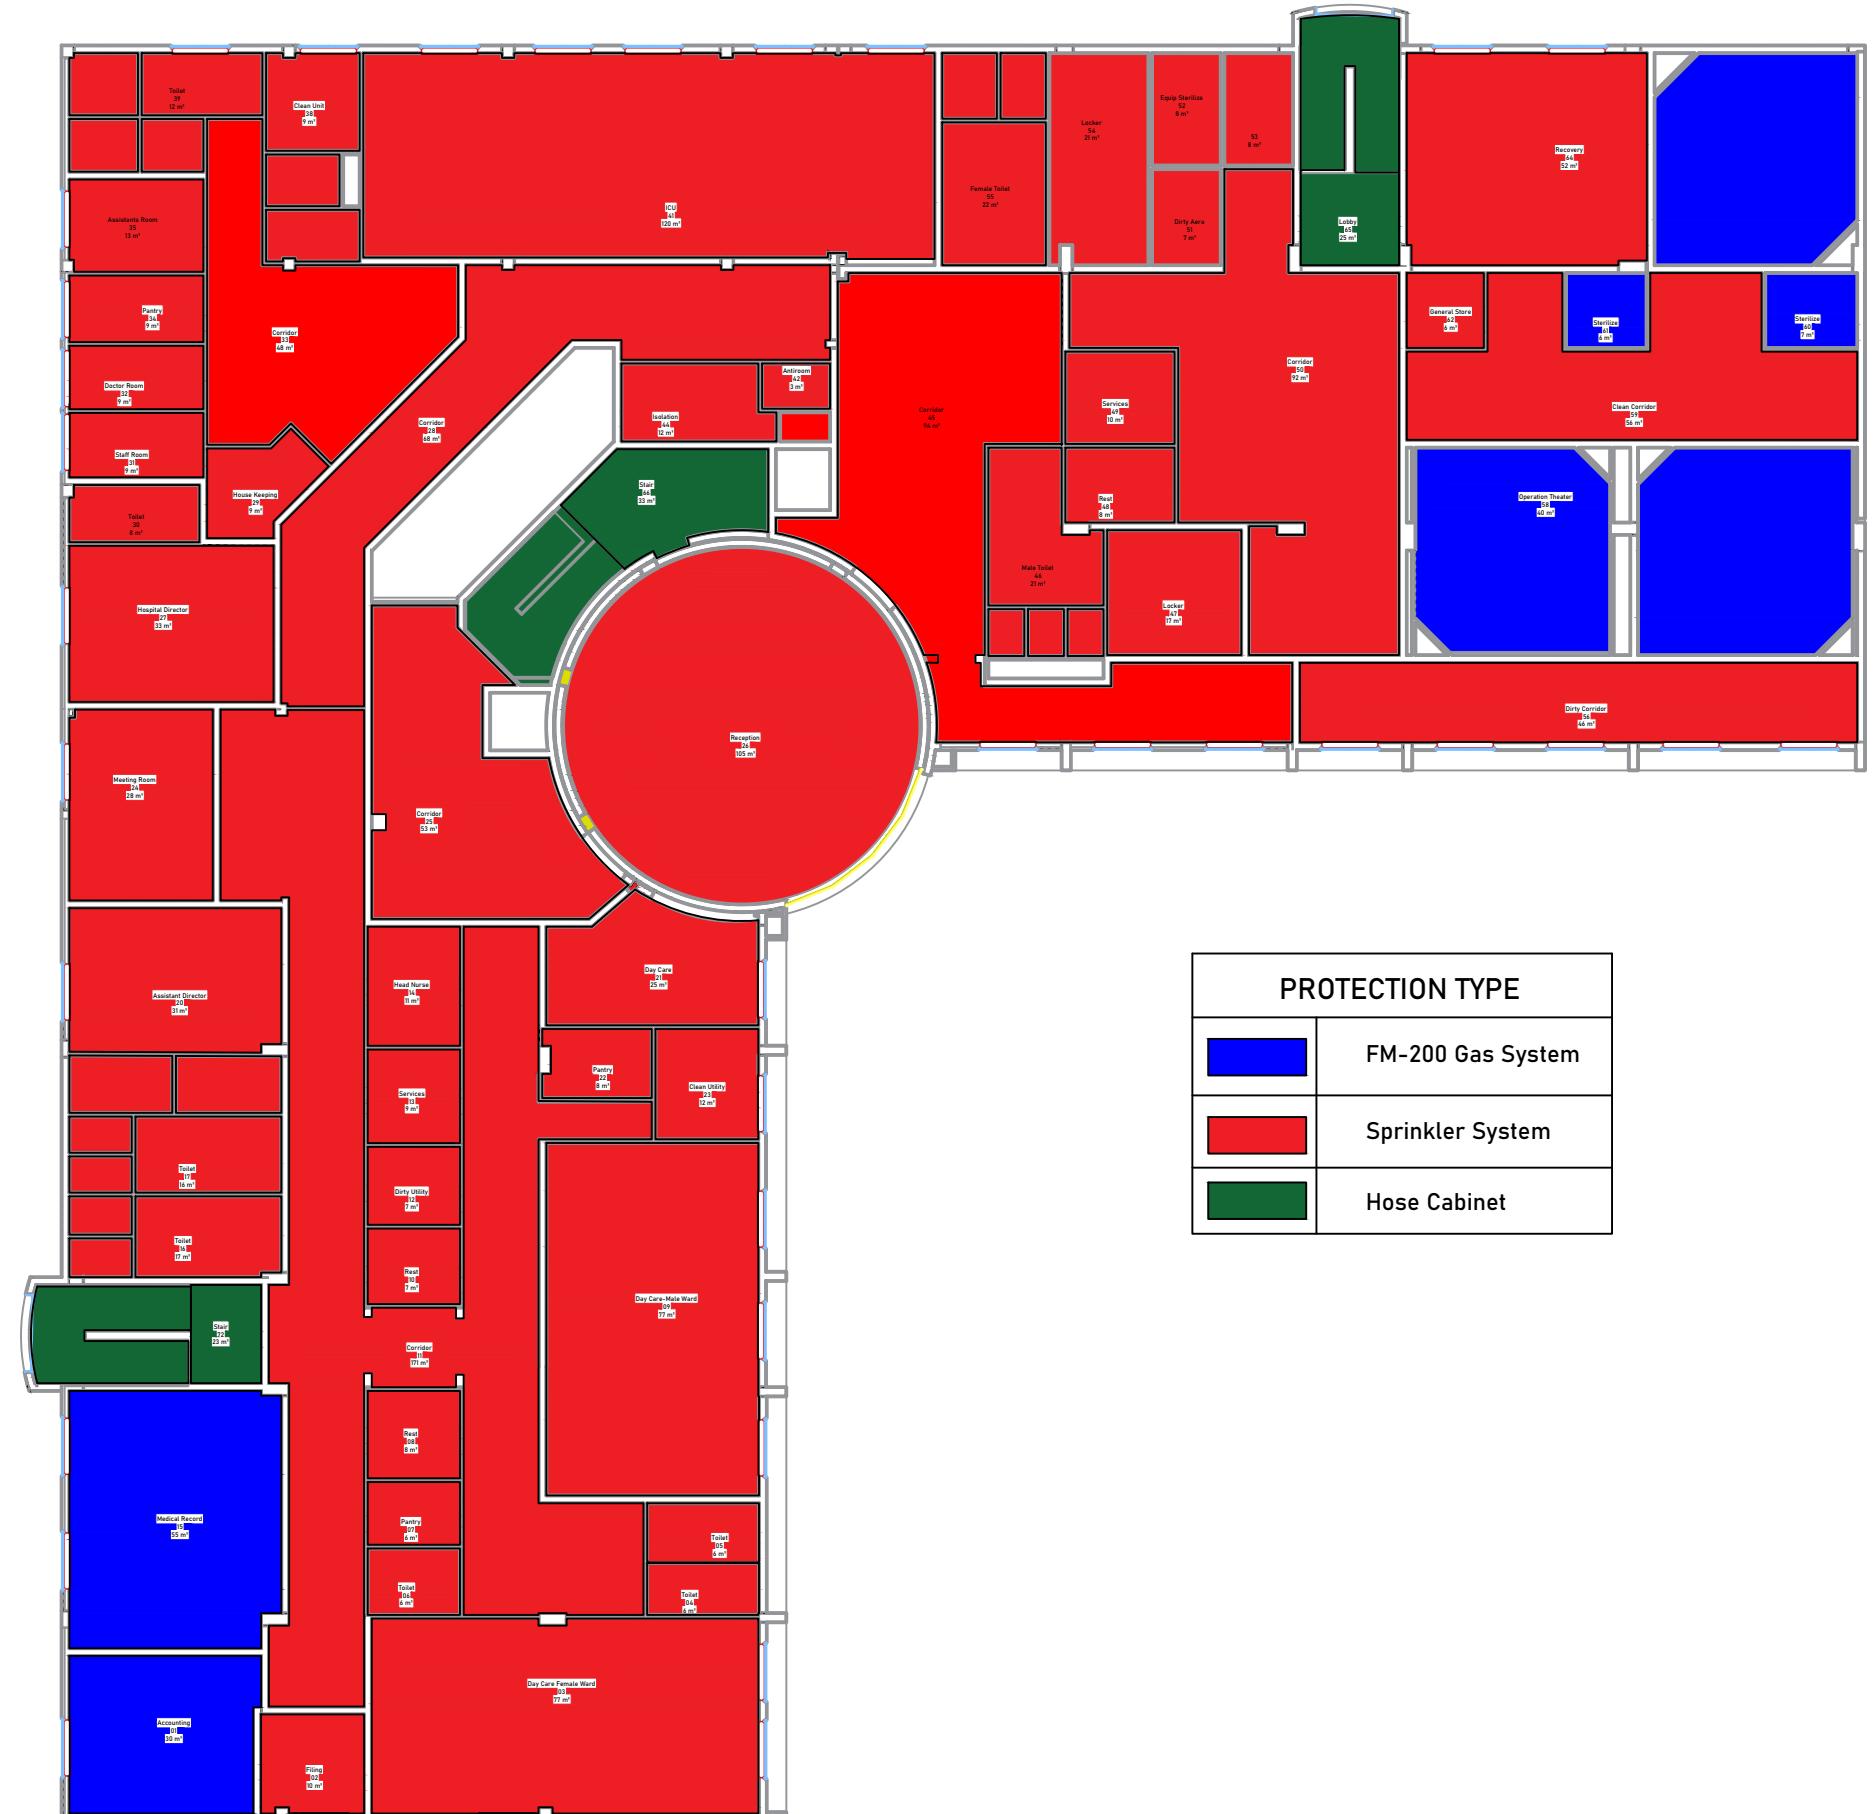

Ground Floor Plan - Fire Fighting System

ASEC OFFICE COPYRIGHT




ATA



01151313481



ataahmed937@gmail.com

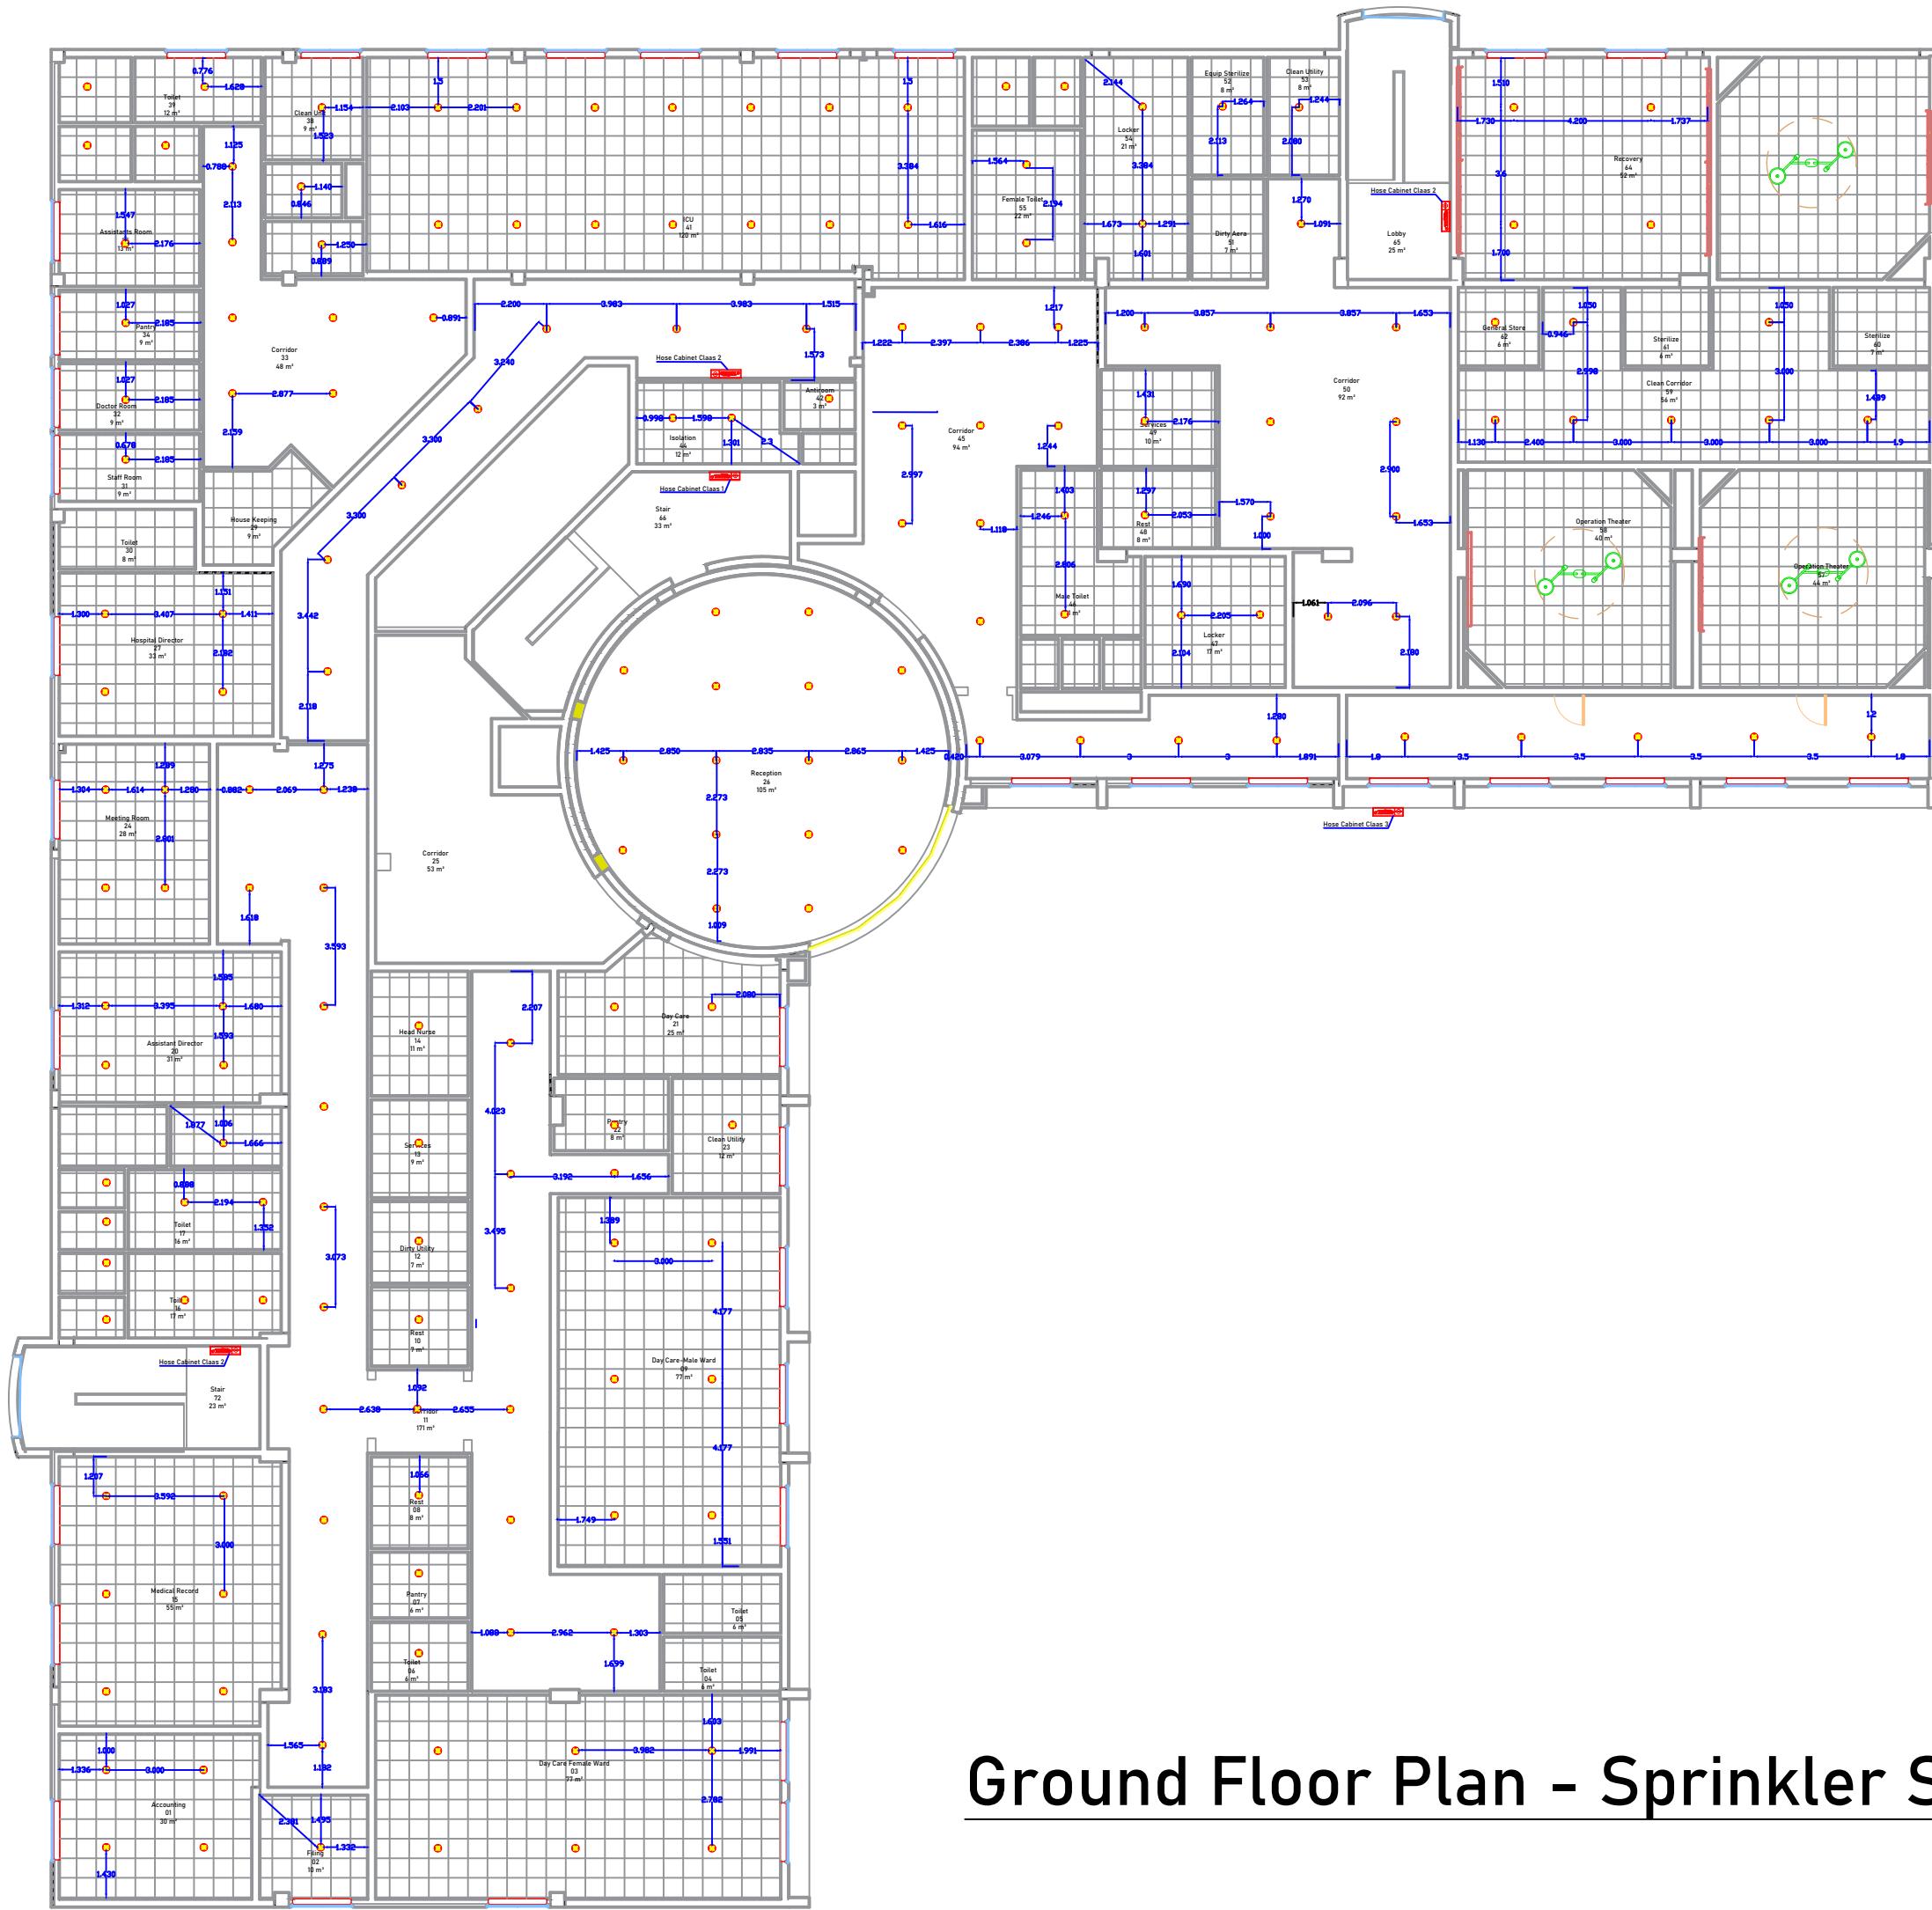

PROJECT NAME
Hospital

SHEET TITLE
Fire Fighting


DESIGN BY
AHMED ATA

CHECKED BY
Ahmed M.Shuhayb
Hassan Waheed

SCALE 1:100 SHEET NO H-01

DATE
14-8-2023

Ground Floor Plan - Sprinkler System

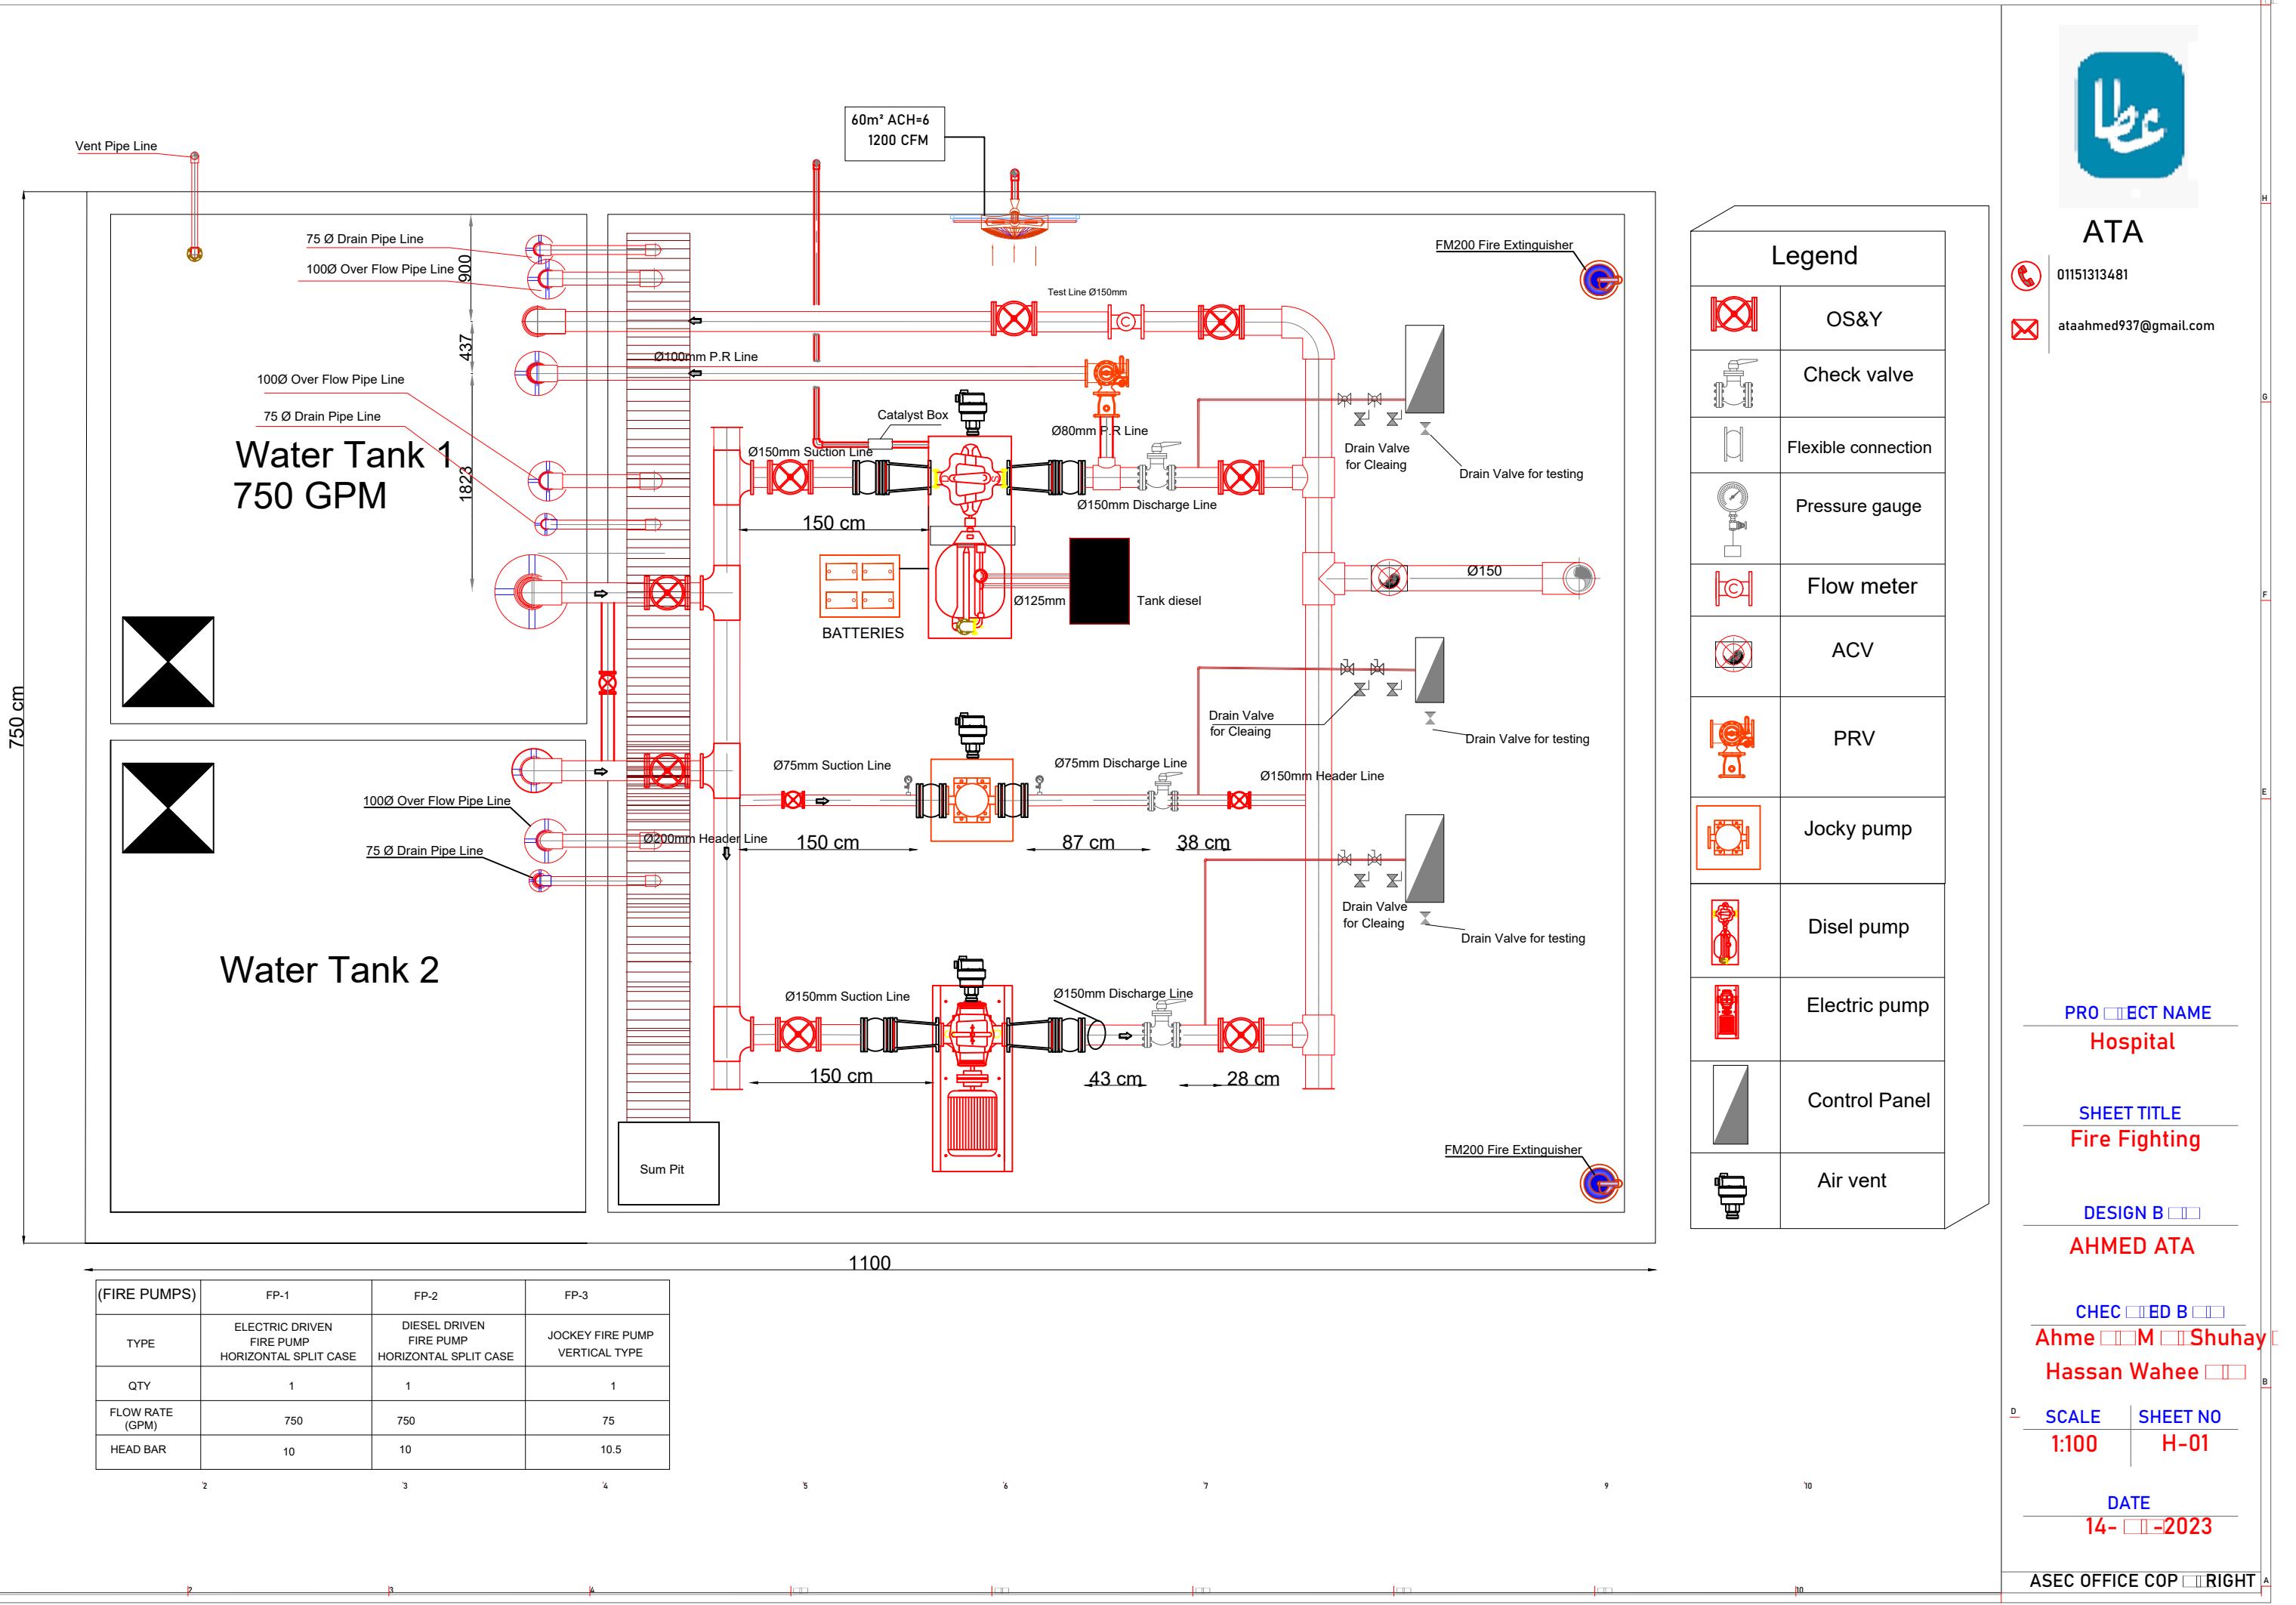


2

3

4

10

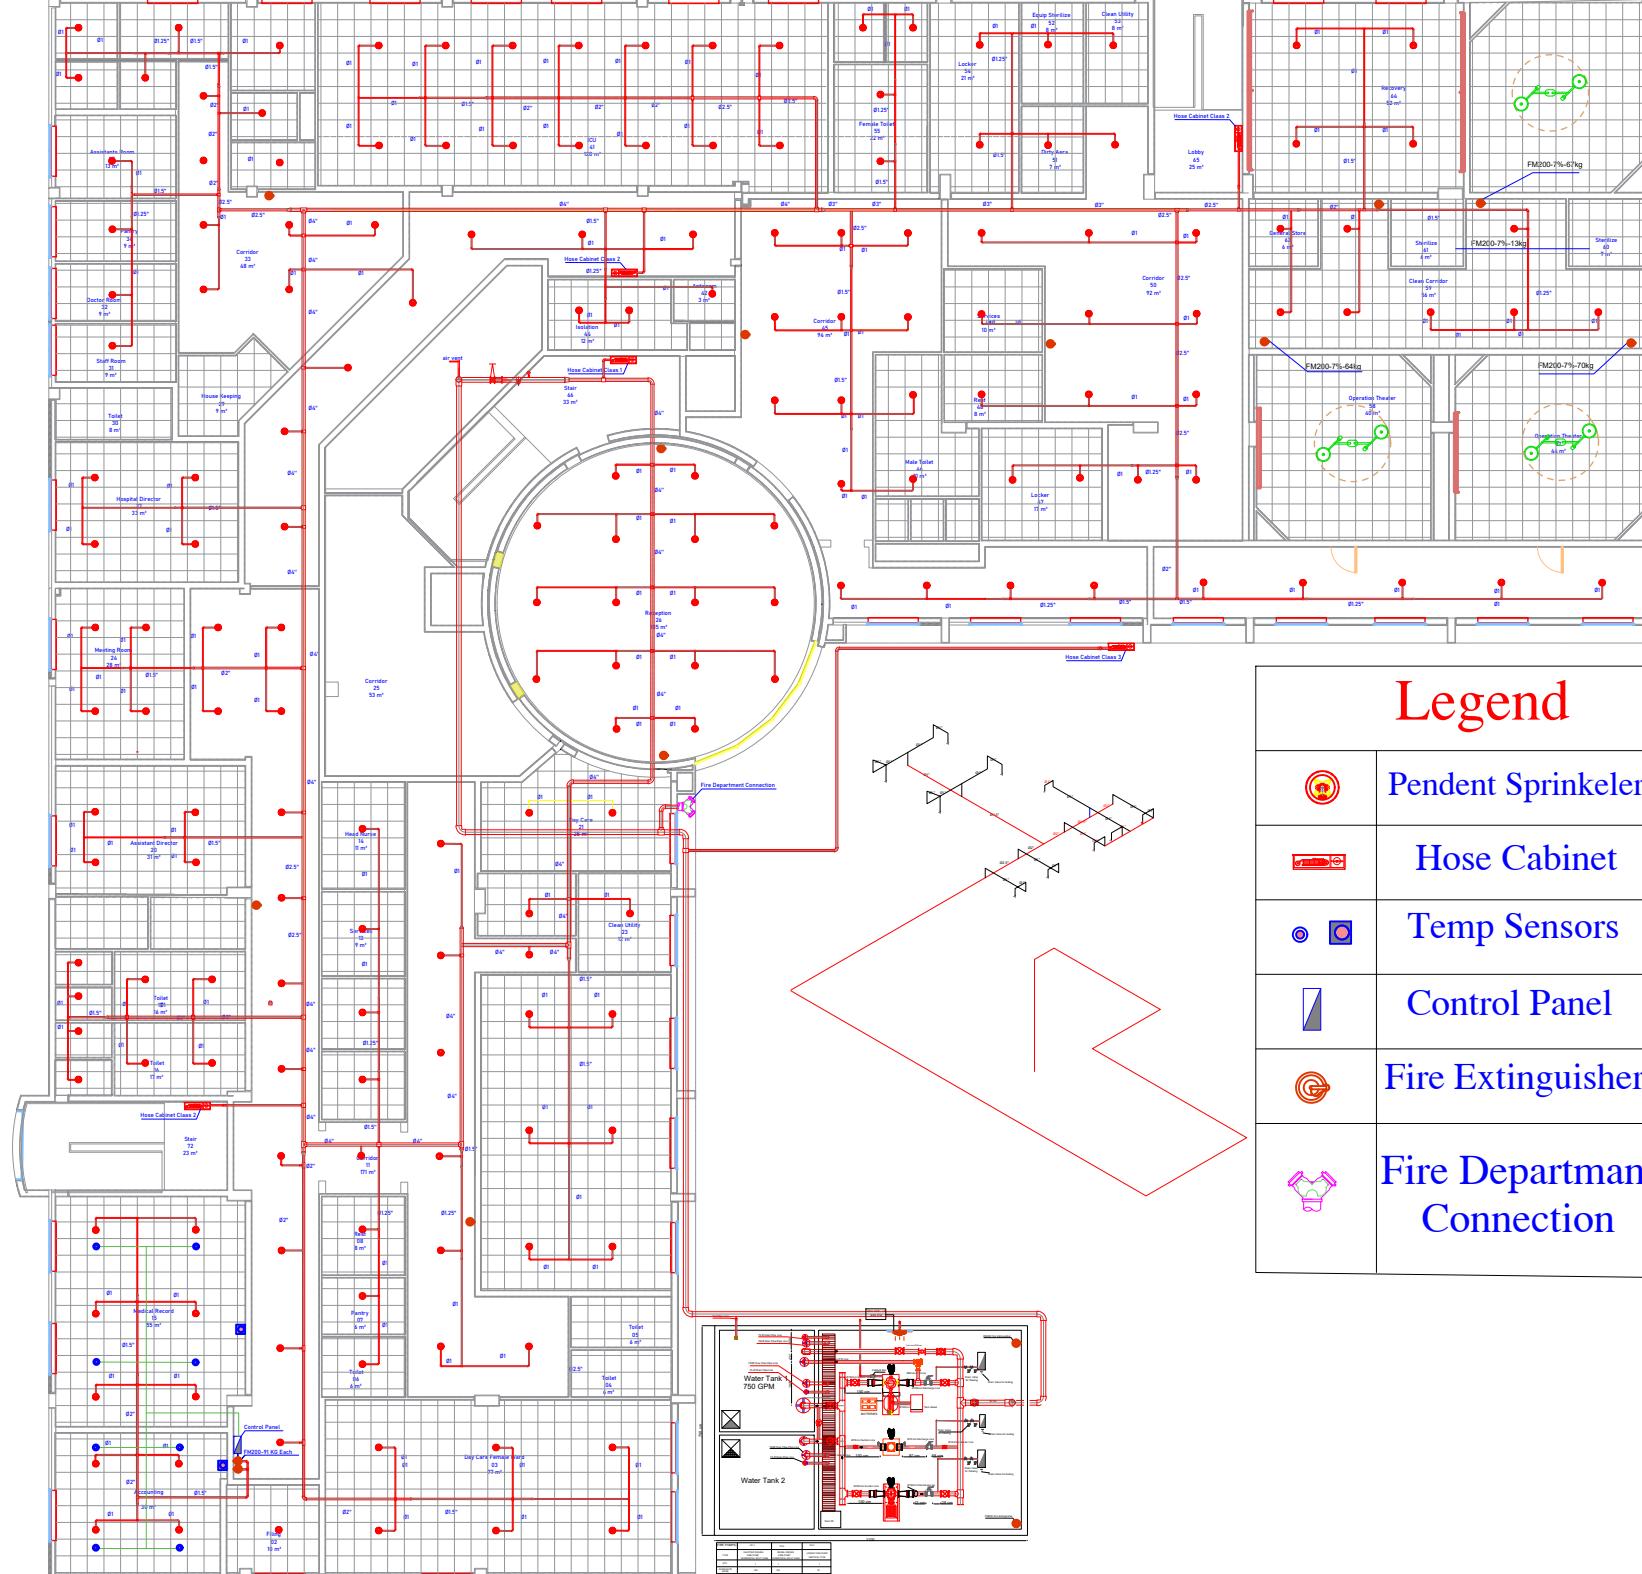

Ground Floor Fire Fighting System

ATA

01151313481

ataahmed937@gmail.com

PROJECT NAME
HospitalSHEET TITLE
Fire FightingDESIGN BY
AHMED ATACHECKED BY
HASSAN WAHEEDSCALE SHEET NO
1:100 H-01DATE
14-02-2023

ASEC OFFICE COPRIGHT A